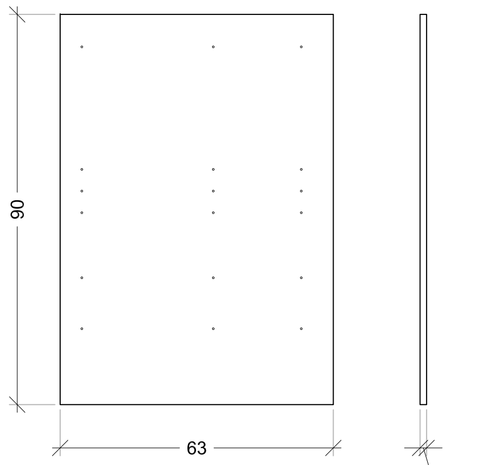

LATI MOBILE BASE X2

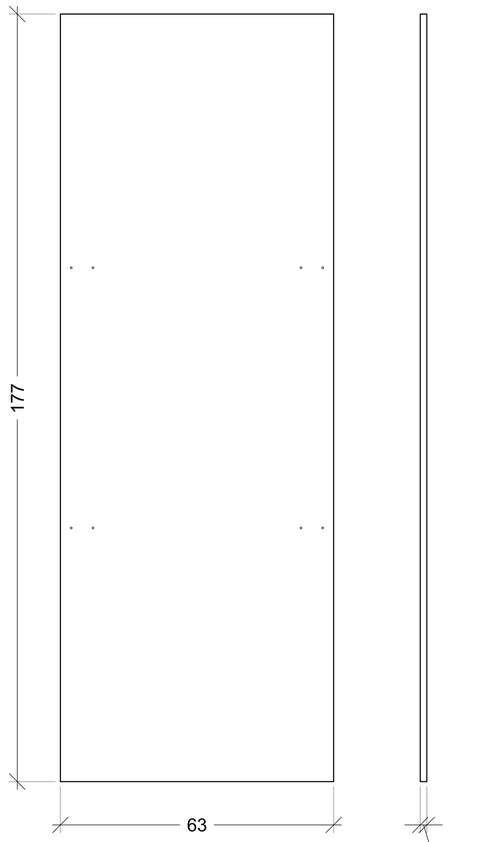

BASE D'APPOGGIO INFERIORE X1

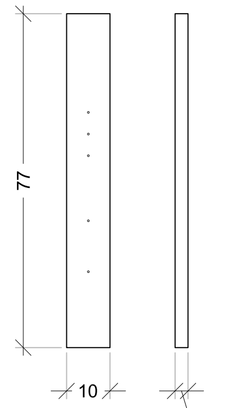

DIVISORIO VERTICALE X4

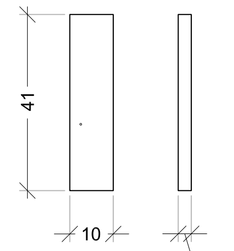

DIVISORIO ORIZZONTALE X4

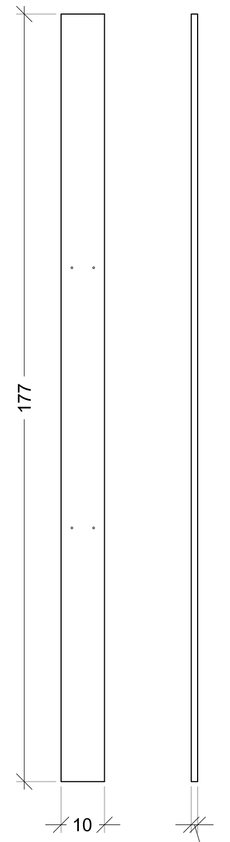

BASE D'APPOGGIO PIANO DA LAVORO X2

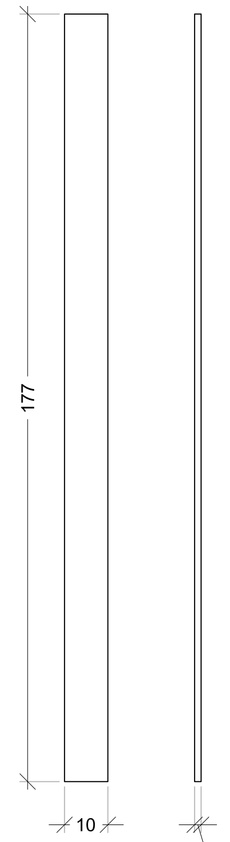

BATTISCOPA X1

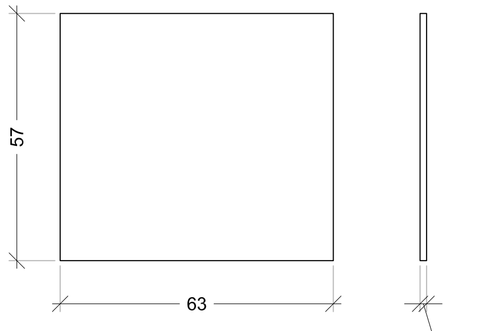

BASE D'APPOGGIO FORNO AD INCASSO X1

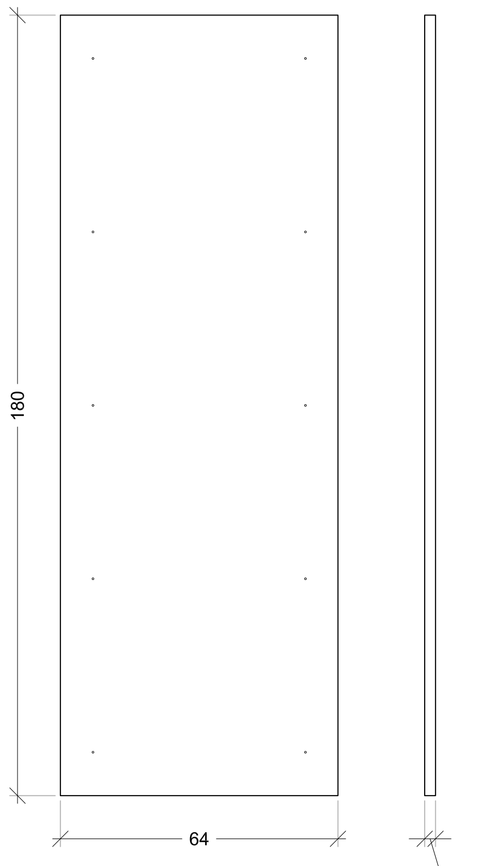

PIANO DA LAVORO X1

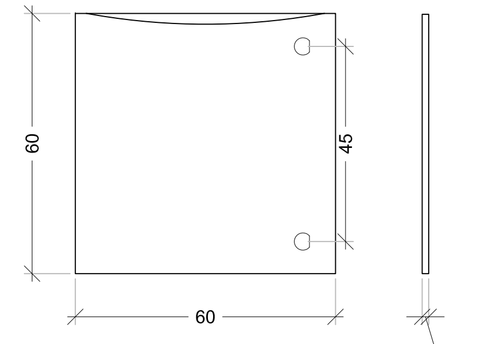

ANTA CENTRALE X1

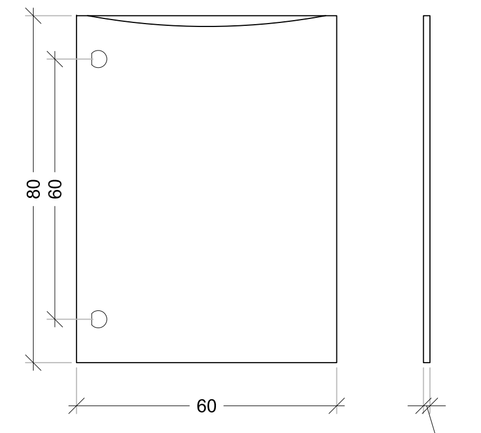

ANTA LATERALE X1

POLITECNICO DI MILANO
SCUOLA DEL DESIGN
C.L. DESIGN DEGLI INTERNI

PROGETTO:

QM-D_1_CUCINA

CORSO:
STRUMENTI E METODI DEL PROGETTO

DOCENTE:
MARCO FERRARA

STUDENTI:
DAVIDE BRANDI

OGGETTO:
MOBILE CUCINA

NOTE:
ABACO DEGLI ELEMENTI

NOME FILE:
KNOXHULT 703.267.88.dwg

VERS	DATA
A	2017/07/18

TAVOLA NO.: **1** DI **6**

A701

DATA: **2017/07/18** SCALA: **1:10**
REV: **A** FORMATO: **A1**

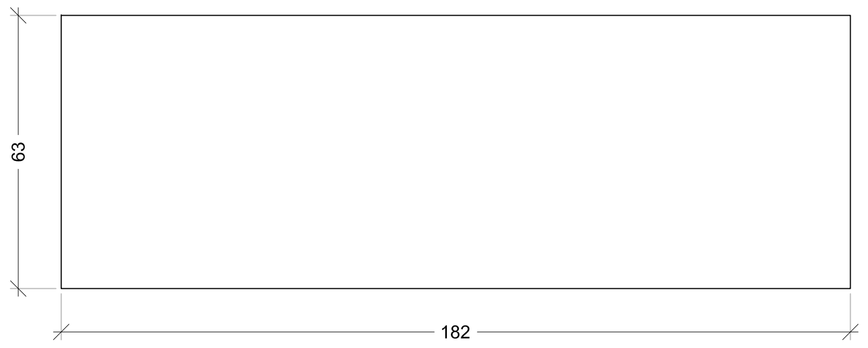

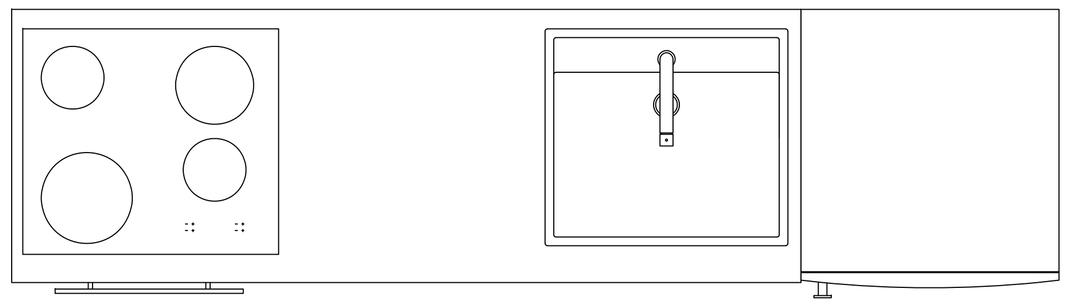

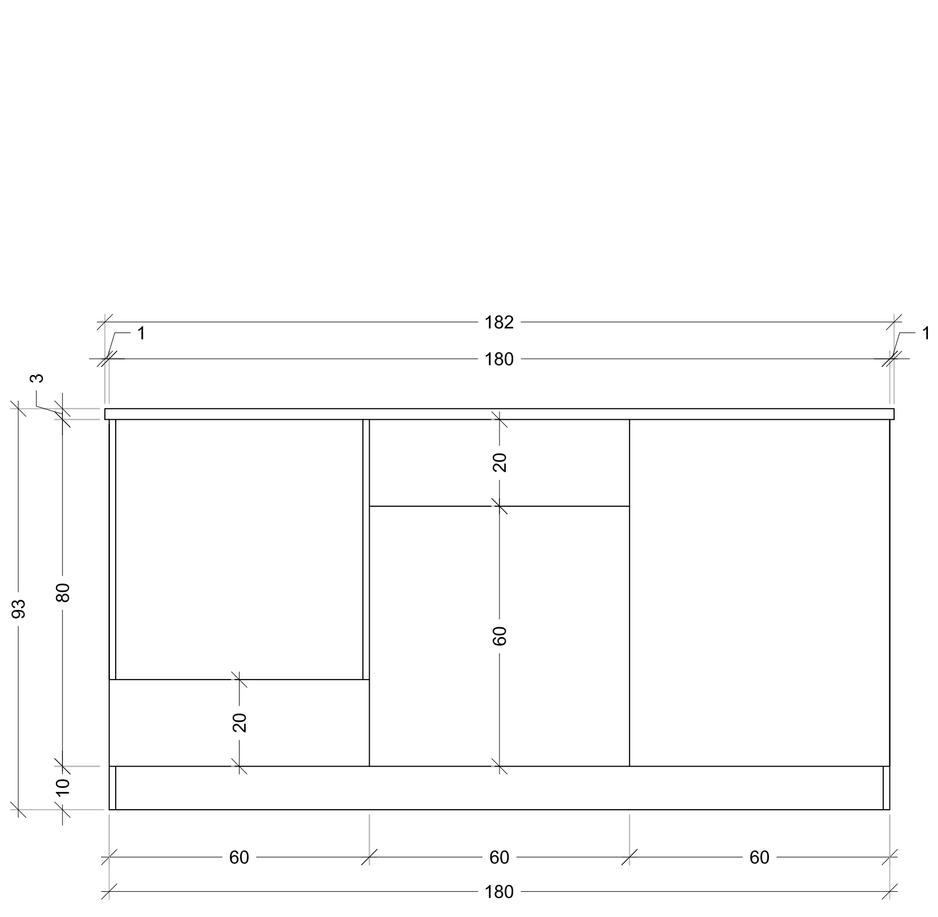

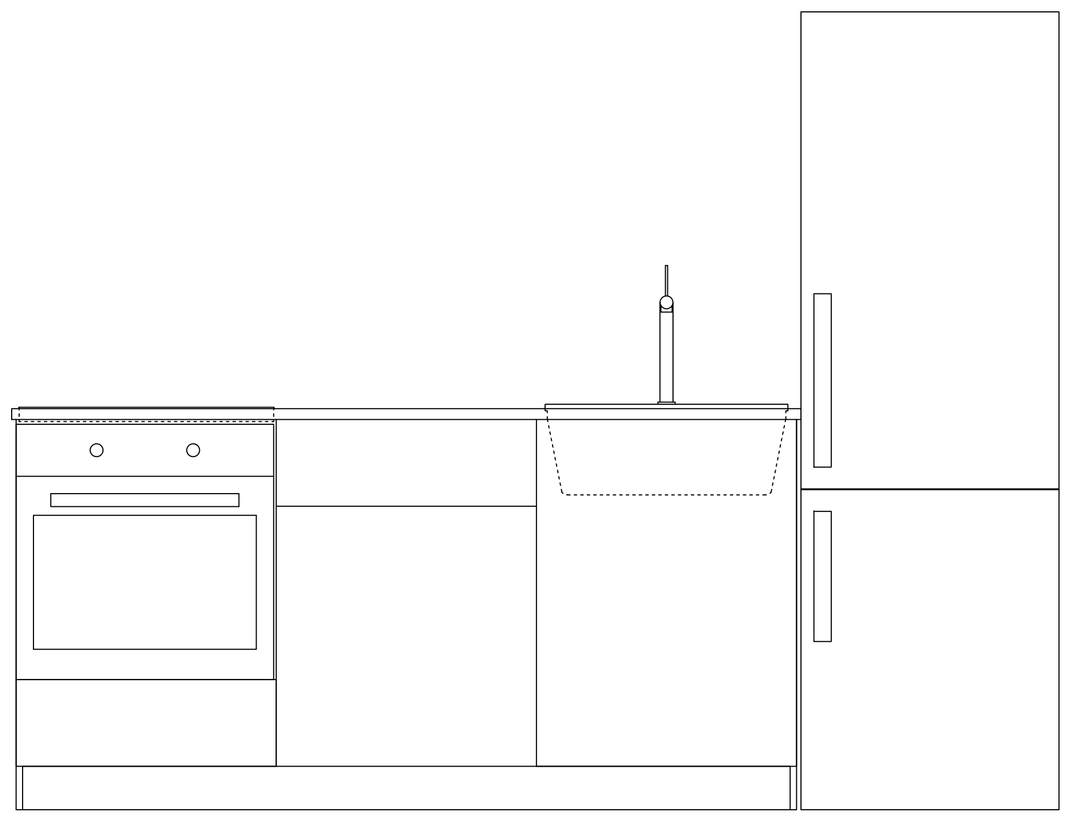

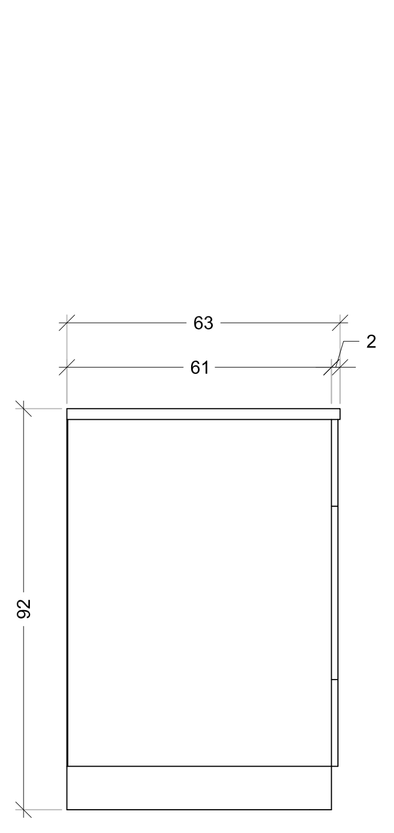

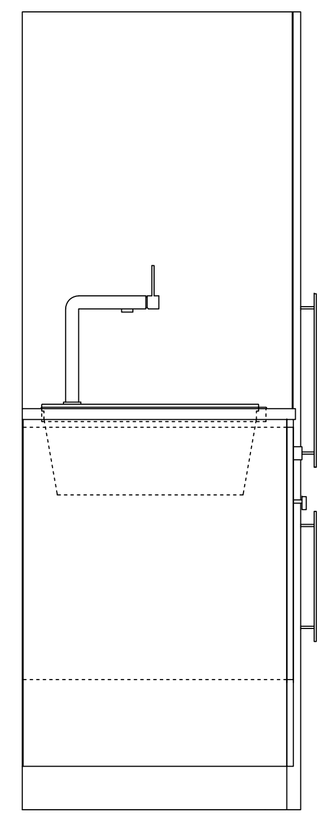

POLITECNICO DI MILANO
SCUOLA DEL DESIGN
C.L. DESIGN DEGLI INTERNI

PROGETTO:

QM-D_1_CUCINA

CORSO:
STRUMENTI E METODI DEL PROGETTO

DOCENTE:
MARCO FERRARA

STUDENTI:
DAVIDE BRANDI

OGGETTO:
MOBILE CUCINA

NOTE:
VISTE PRINCIPALI CUCINA E INGOMBRO ACCESSORI

NOME FILE:
KNOXHULT 703.267.88.dwg

VERS	DATA
A	**2017/07/18**

TAVOLA NO.: **2 DI 6**

A702

DATA: **2017/07/18** SCALA: **1:10**
REV: **A** FORMATO: **A1**

DIRECTORY: C:\USERS\UTENTE\DOCUMENTS\GITHUB\QM-D_1_CUCINA\KNOXHULT 703.267.88\KNOXHULT 703.267.88.DWG | PLOTTED ON: 18/07/2017 07:20:36 | BY USER: DAVIDE BRANDI

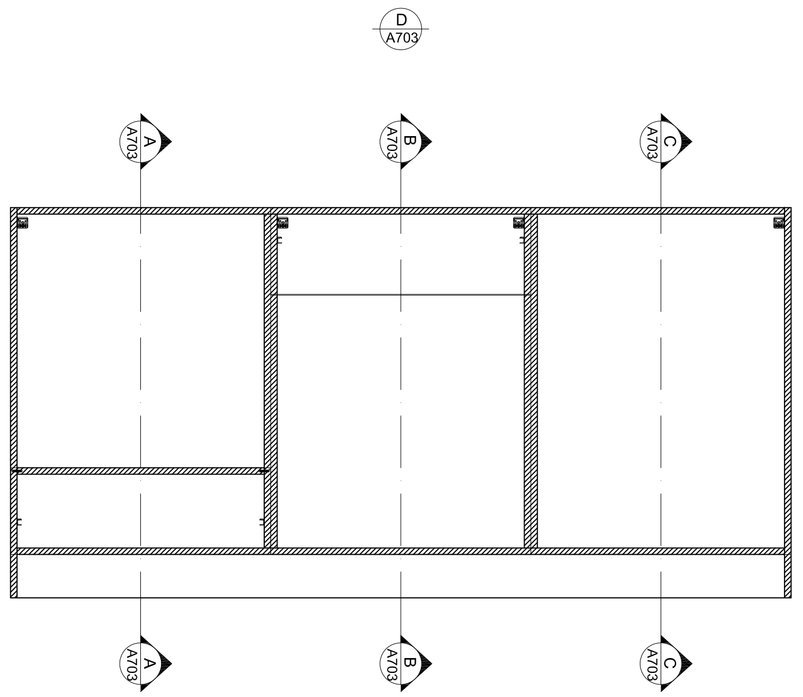

VISTA FRONTALE SEZIONATA

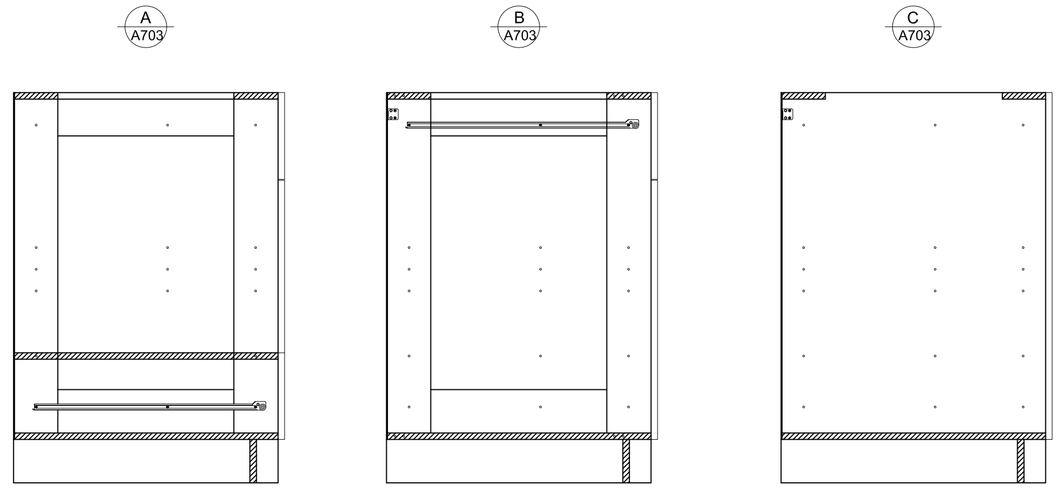

VISTE LATERALI SEZIONATE

CASSETTO

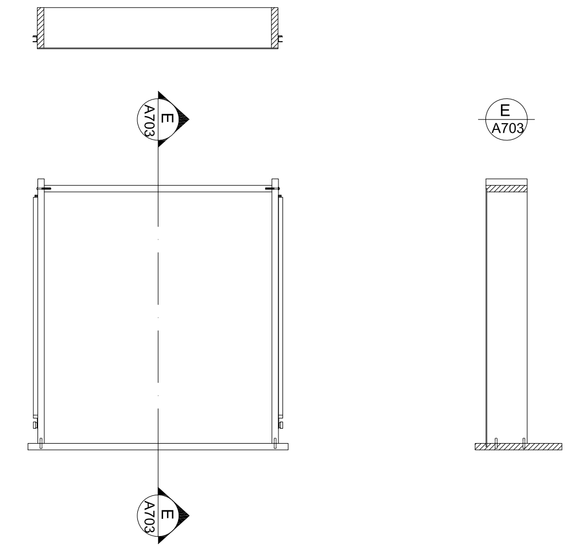

VISTA DALL'ALTO

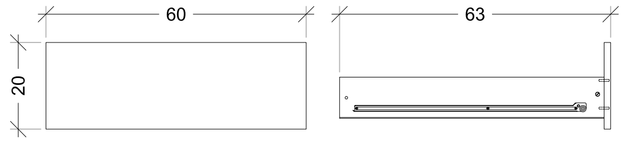

VISTA FRONTALE

VISTA LATERALE

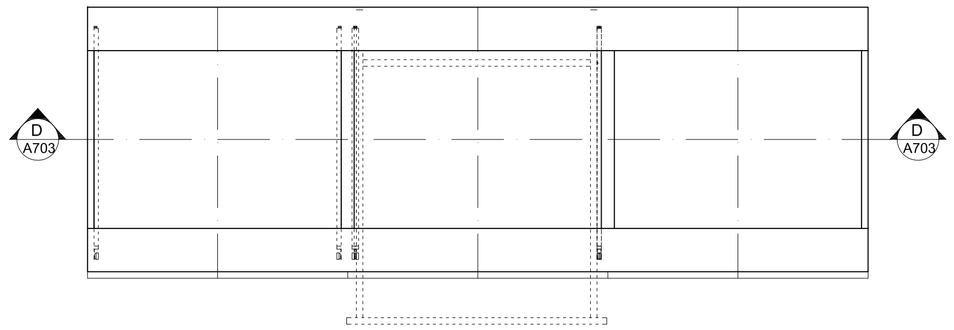

VISTA DALL'ALTO

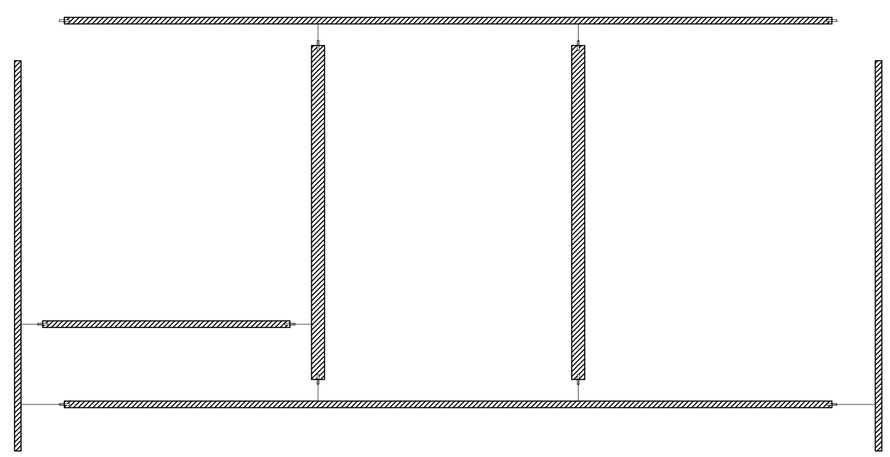

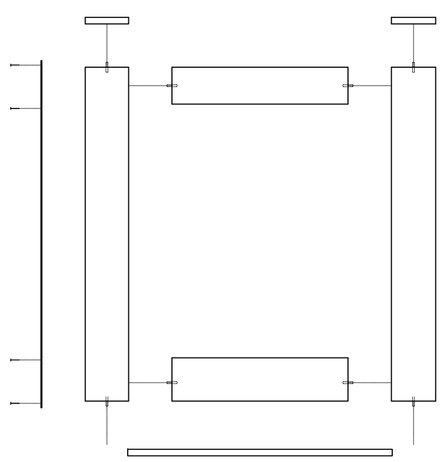

POLITECNICO DI MILANO
SCUOLA DEL DESIGN
C.L. DESIGN DEGLI INTERNI

PROGETTO:

QM-D_1_CUCINA

CORSO:
STRUMENTI E METODI DEL PROGETTO

DOCENTE:
MARCO FERRARA

STUDENTI:
DAVIDE BRANDI

OGGETTO:
MOBILE CUCINA

NOTE:
SEZIONI CUCINA E CASSETTO

NOME FILE:
KNOXHULT 703.267.88.dwg

VERS	DATA
A	**2017/07/18**

TAVOLA NO.: **3 DI 6**

A703

DATA: **2017/07/18** SCALA: **1:10**
REV: **A** FORMATO: **A1**

DIRECTORY: C:\USERS\UTENTE\DOCUMENTS\GITHUB\QM-D_1_CUCINA\KNOXHULT 703.267.88\KNOXHULT 703.267.88.DWG | PLOTTED ON: 18/07/2017 07:20:49 | BY USER: DAVIDE BRANDI